


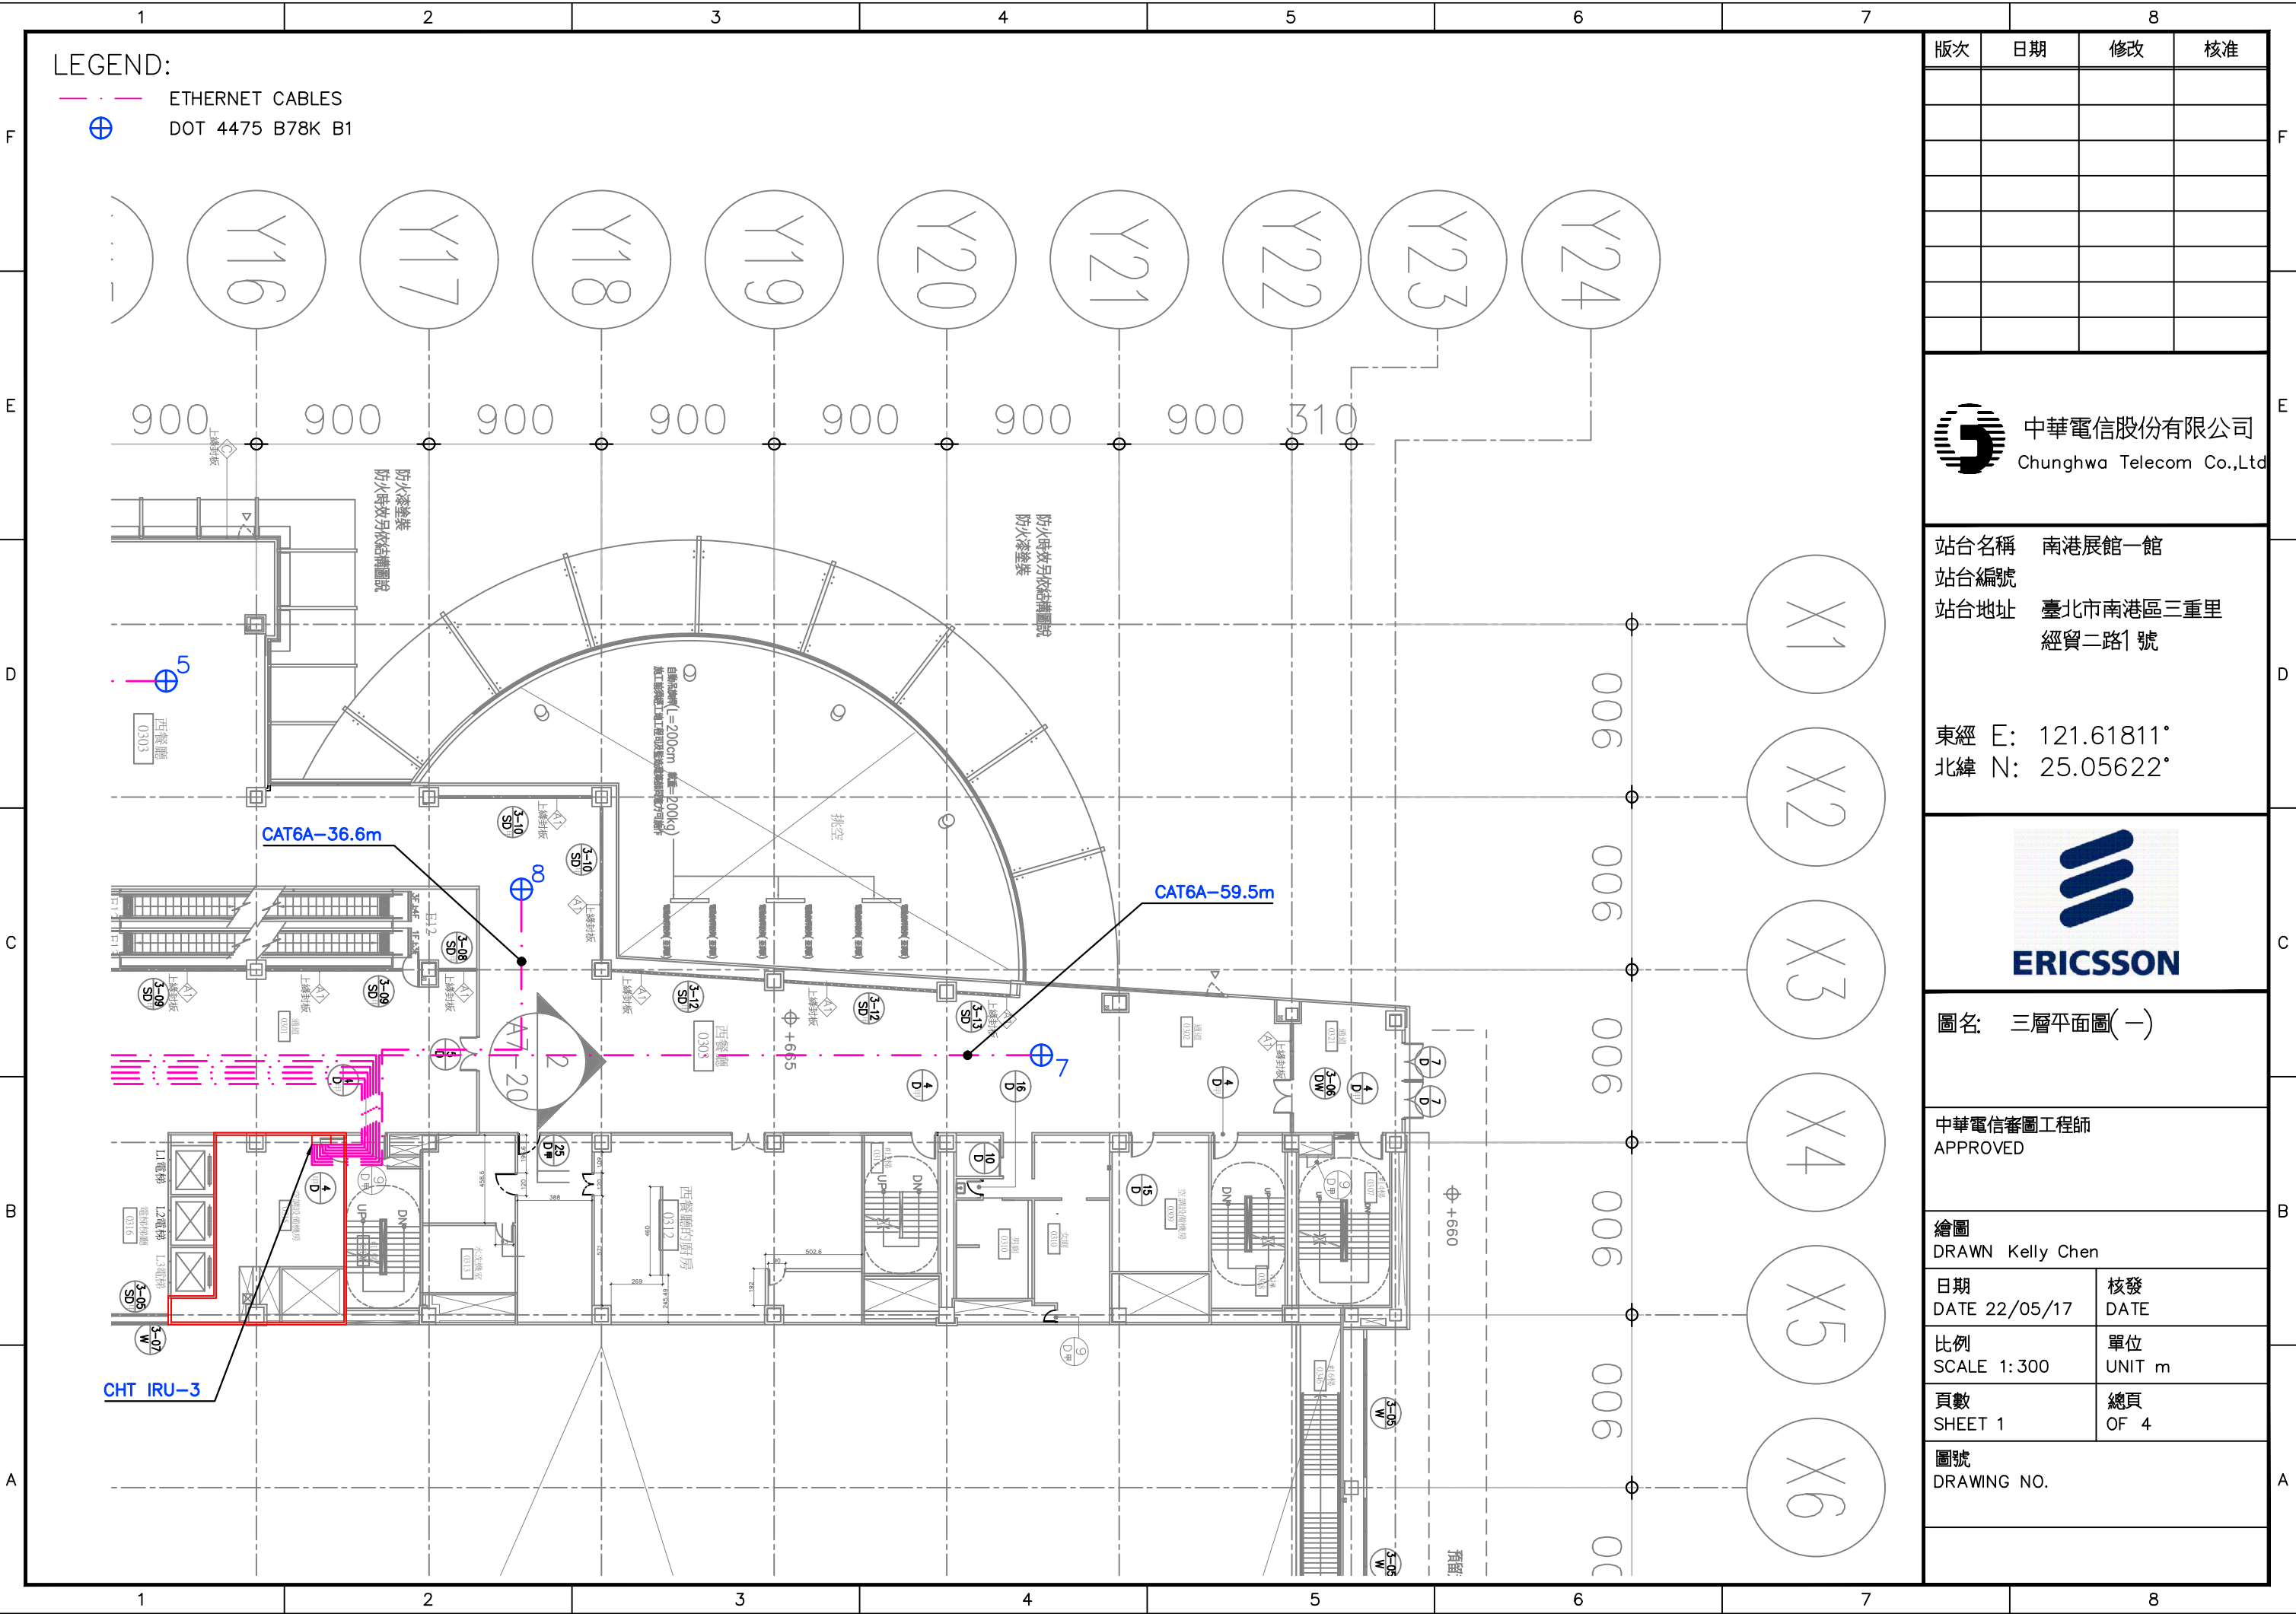


LEGEND:

ETHERNET CABLES

DOT 4475 B78K B1

版次	日期	修改	核准

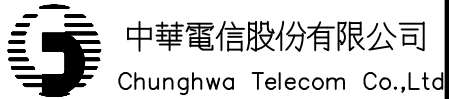

站名名稱 南港展館一館

站台編號

站台地址 臺北市南港區三重里
經貿二路1號

東經 E: 121.61811°

北緯 N: 25.05622°



圖名: 三層平面圖(一)

中華電信審圖工程師
APPROVED


繪圖
DRAWN Kelly Chen

日期 DATE 22/05/17	核發 DATE
---------------------	------------

比例 SCALE 1: 300	單位 UNIT m
--------------------	--------------


頁數 SHEET 1	總頁 OF 4
---------------	------------

圖號
DRAWING NO.

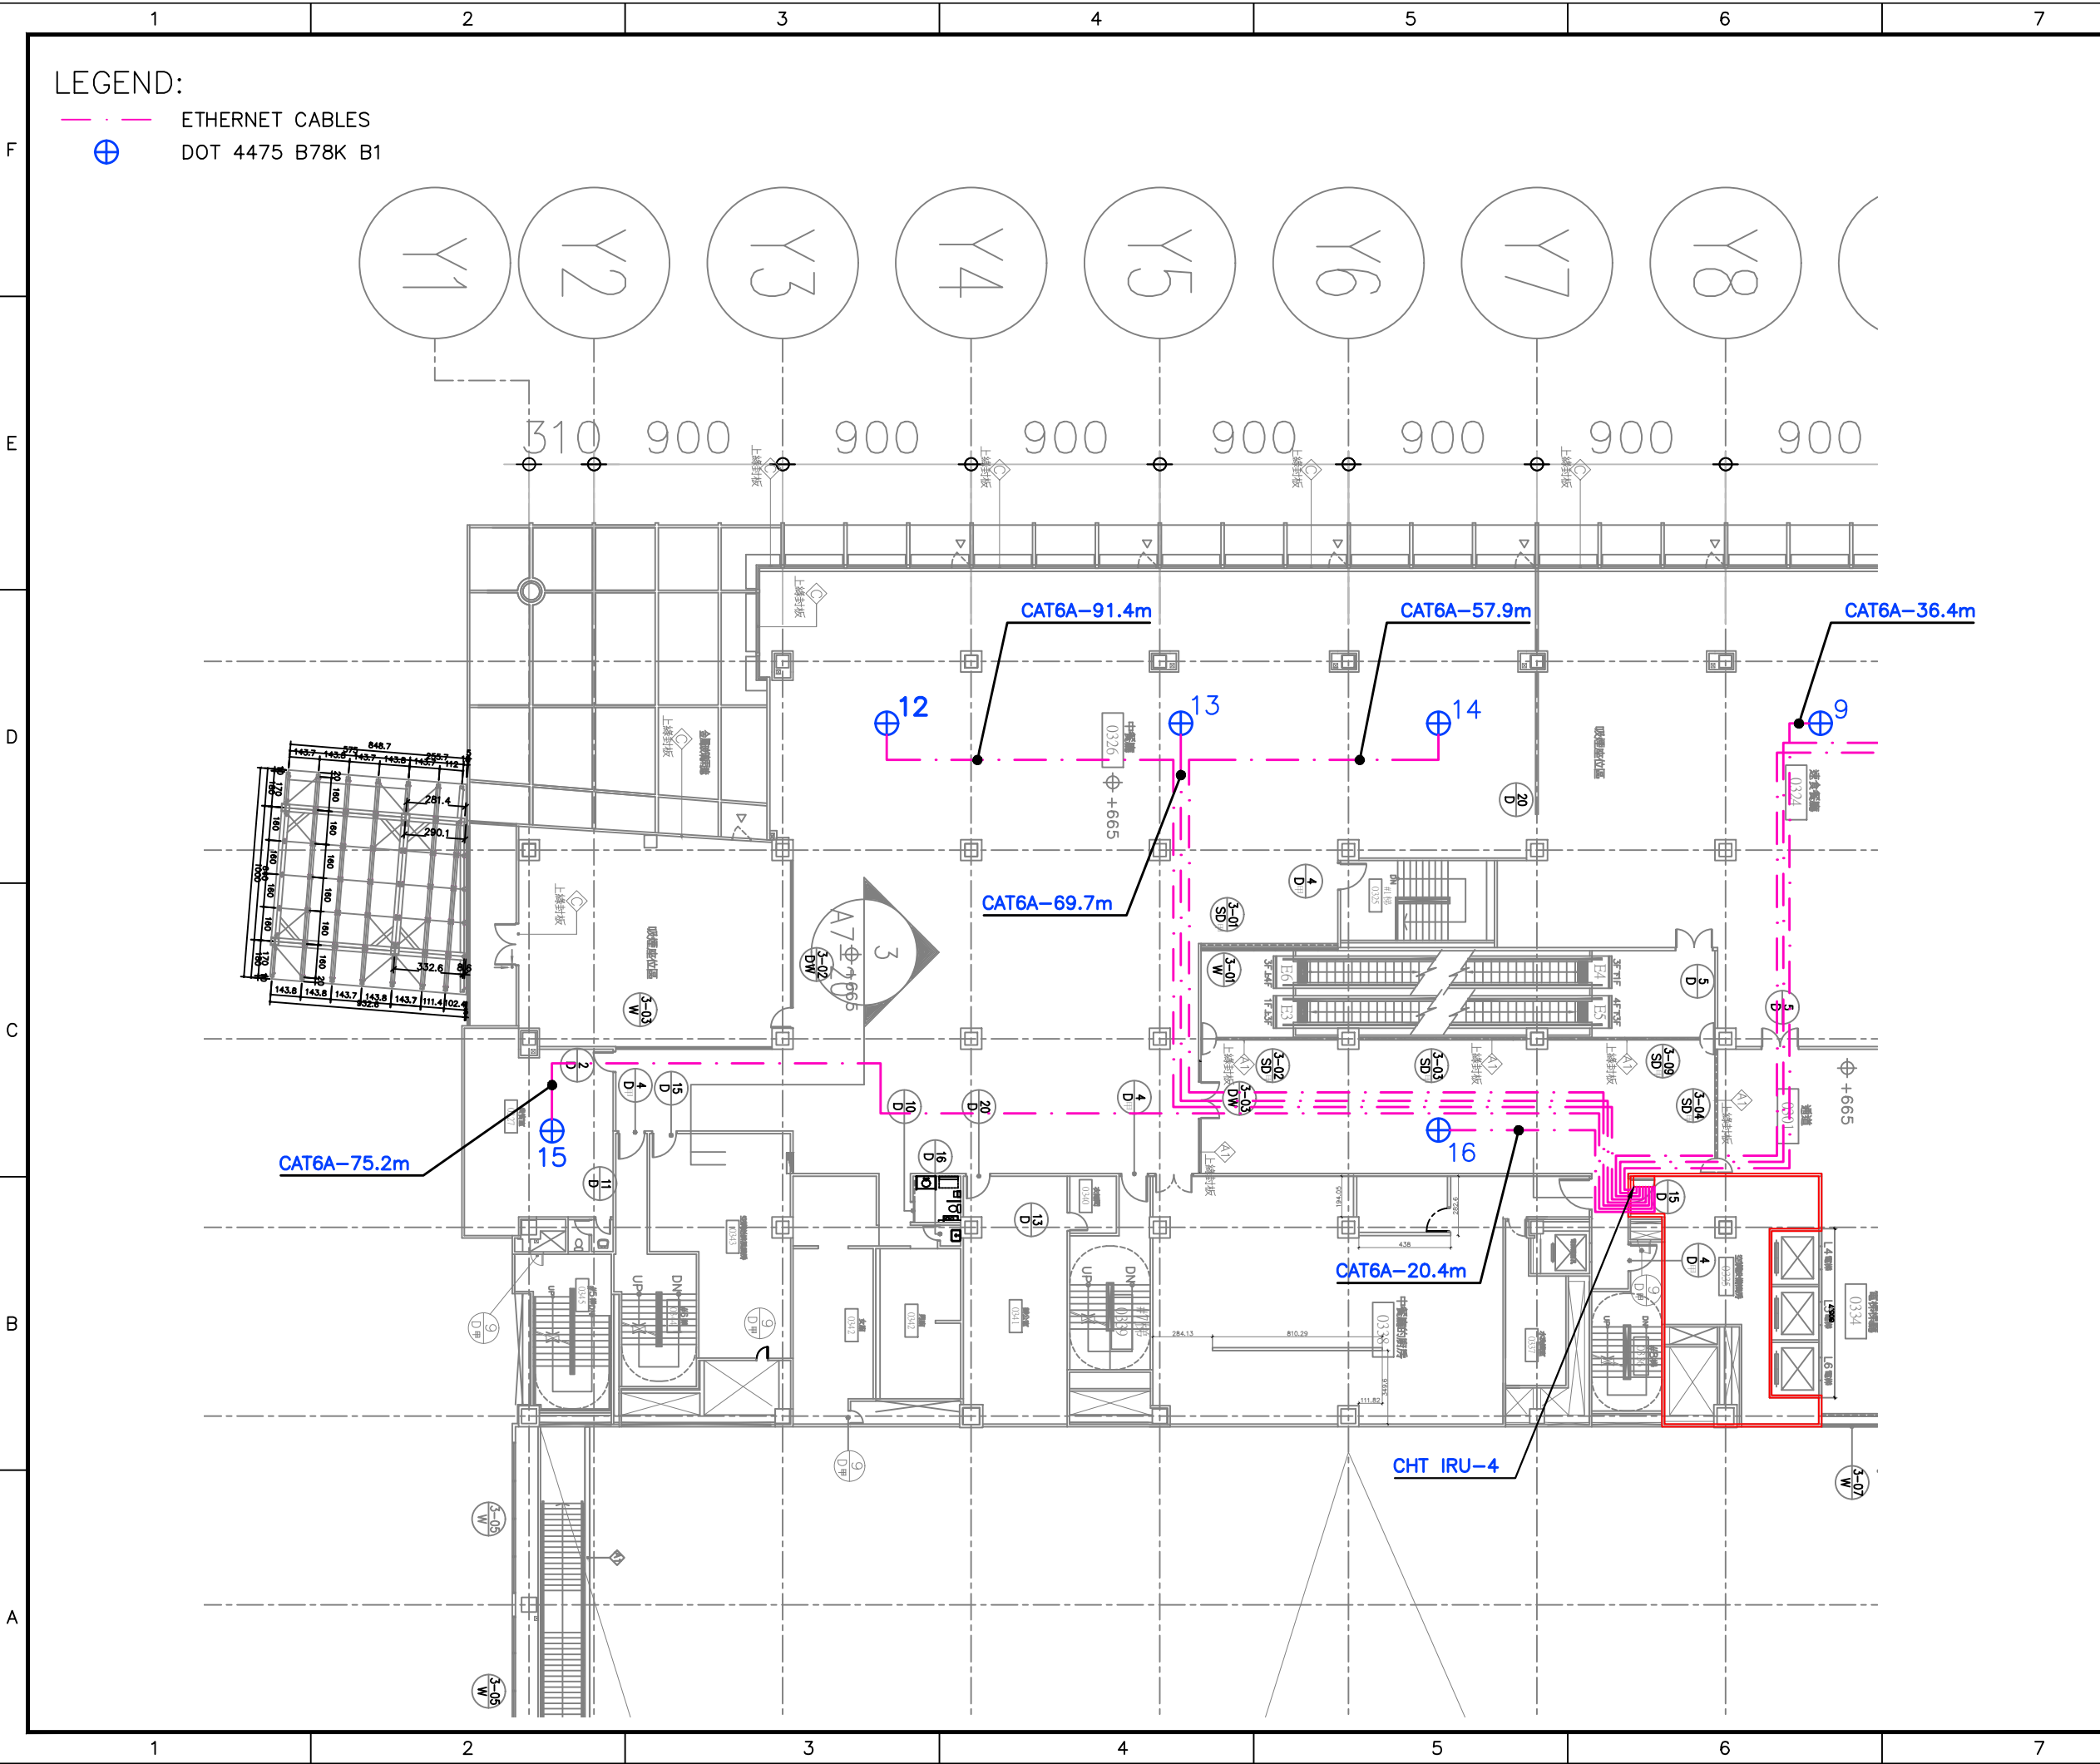

LEGEND:
ETHERNET CABLES
DOT 4475 B78K B1

版次	日期	修改	核准

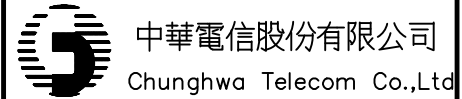

站名名稱 南港展館一館
站名編號
站名地址 臺北市南港區三重里
經貿二路1 號

東經 E: 121.61811°
北緯 N: 25.05622°



圖名: 三層平面圖(三)

中華電信審圖工程師
APPROVED

繪圖
DRAWN Kelly Chen

日期 DATE 22/05/17	核發 DATE
---------------------	------------

比例 SCALE 1: 300	單位 UNIT m
--------------------	--------------

頁數 SHEET 3	總頁 OF 4
---------------	------------

圖號
DRAWING NO.

