



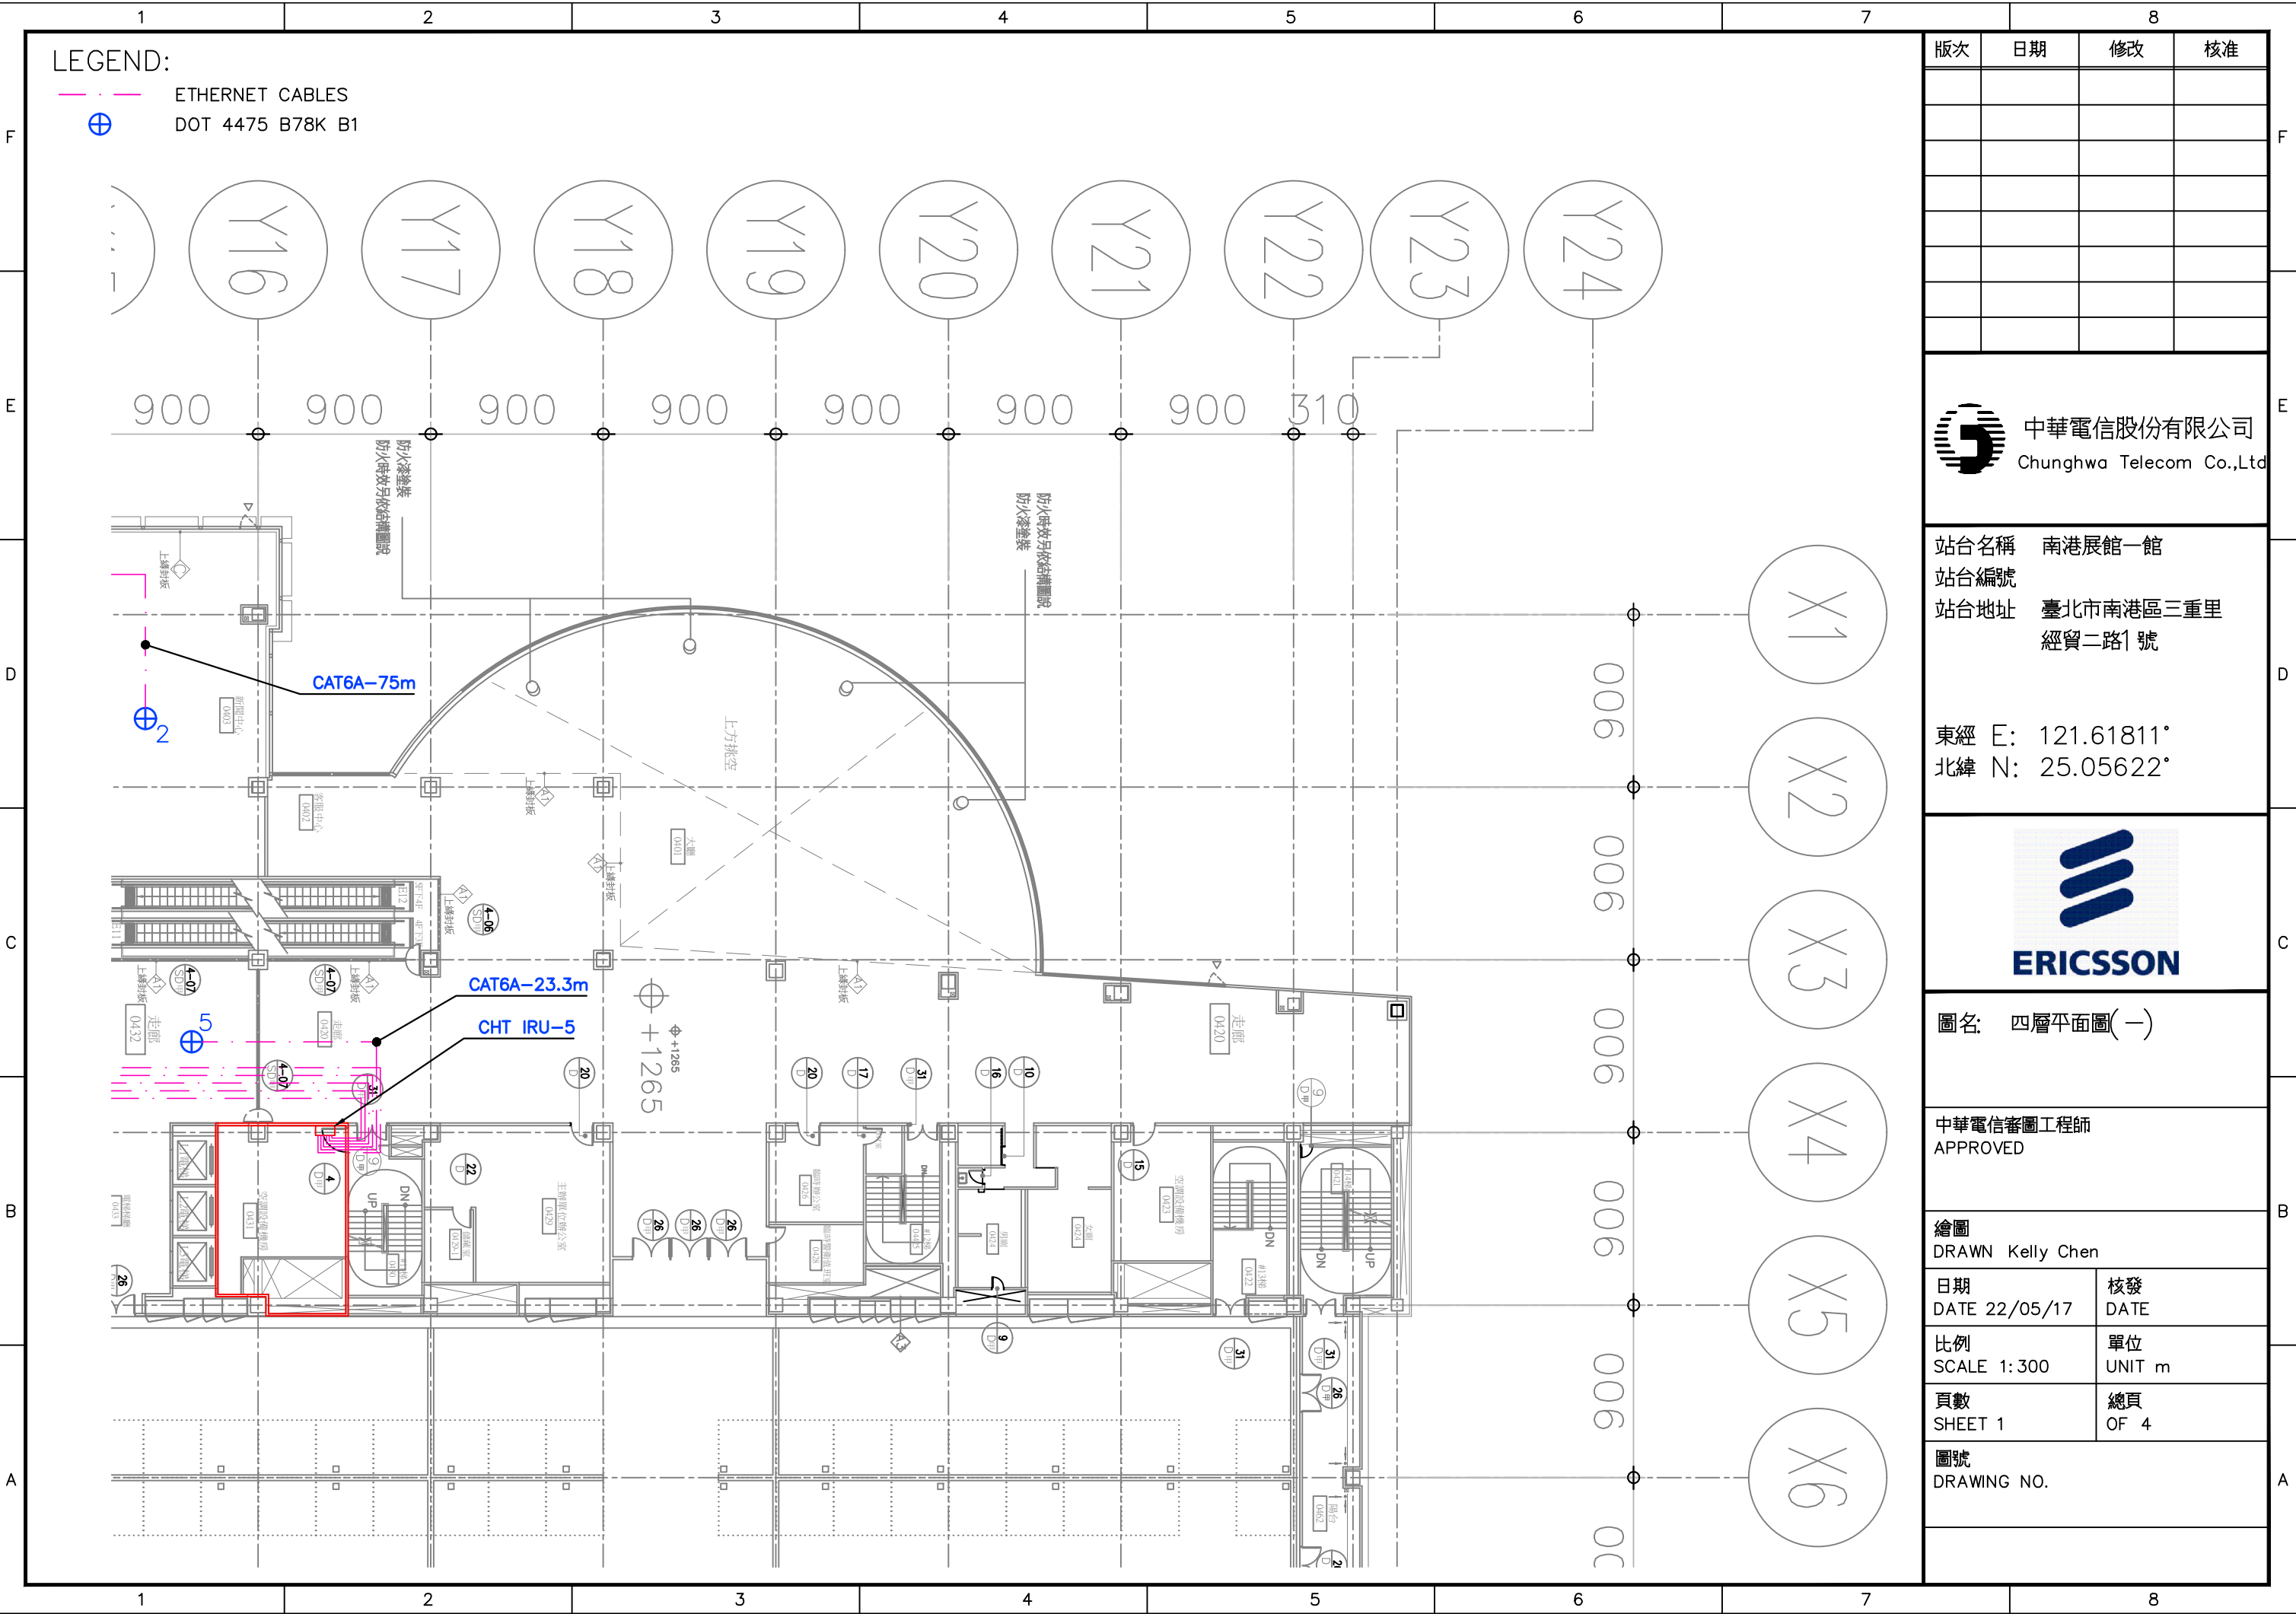

版次	日期	修改	核准

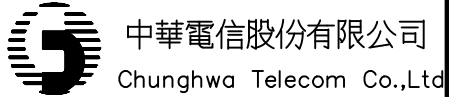

站名名稱 南港展館一館
站名編號
站名地址 臺北市南港區三重里
經貿二路1 號

東經 E: 121.61811°
北緯 N: 25.05622°



圖名: 四層平面圖(一)

中華電信審圖工程師
APPROVED


繪圖
DRAWN Kelly Chen

日期 DATE 22/05/17	核發 DATE
---------------------	------------

比例 SCALE 1: 300	單位 UNIT m
--------------------	--------------

頁數 SHEET 1	總頁 OF 4
---------------	------------

圖號
DRAWING NO.

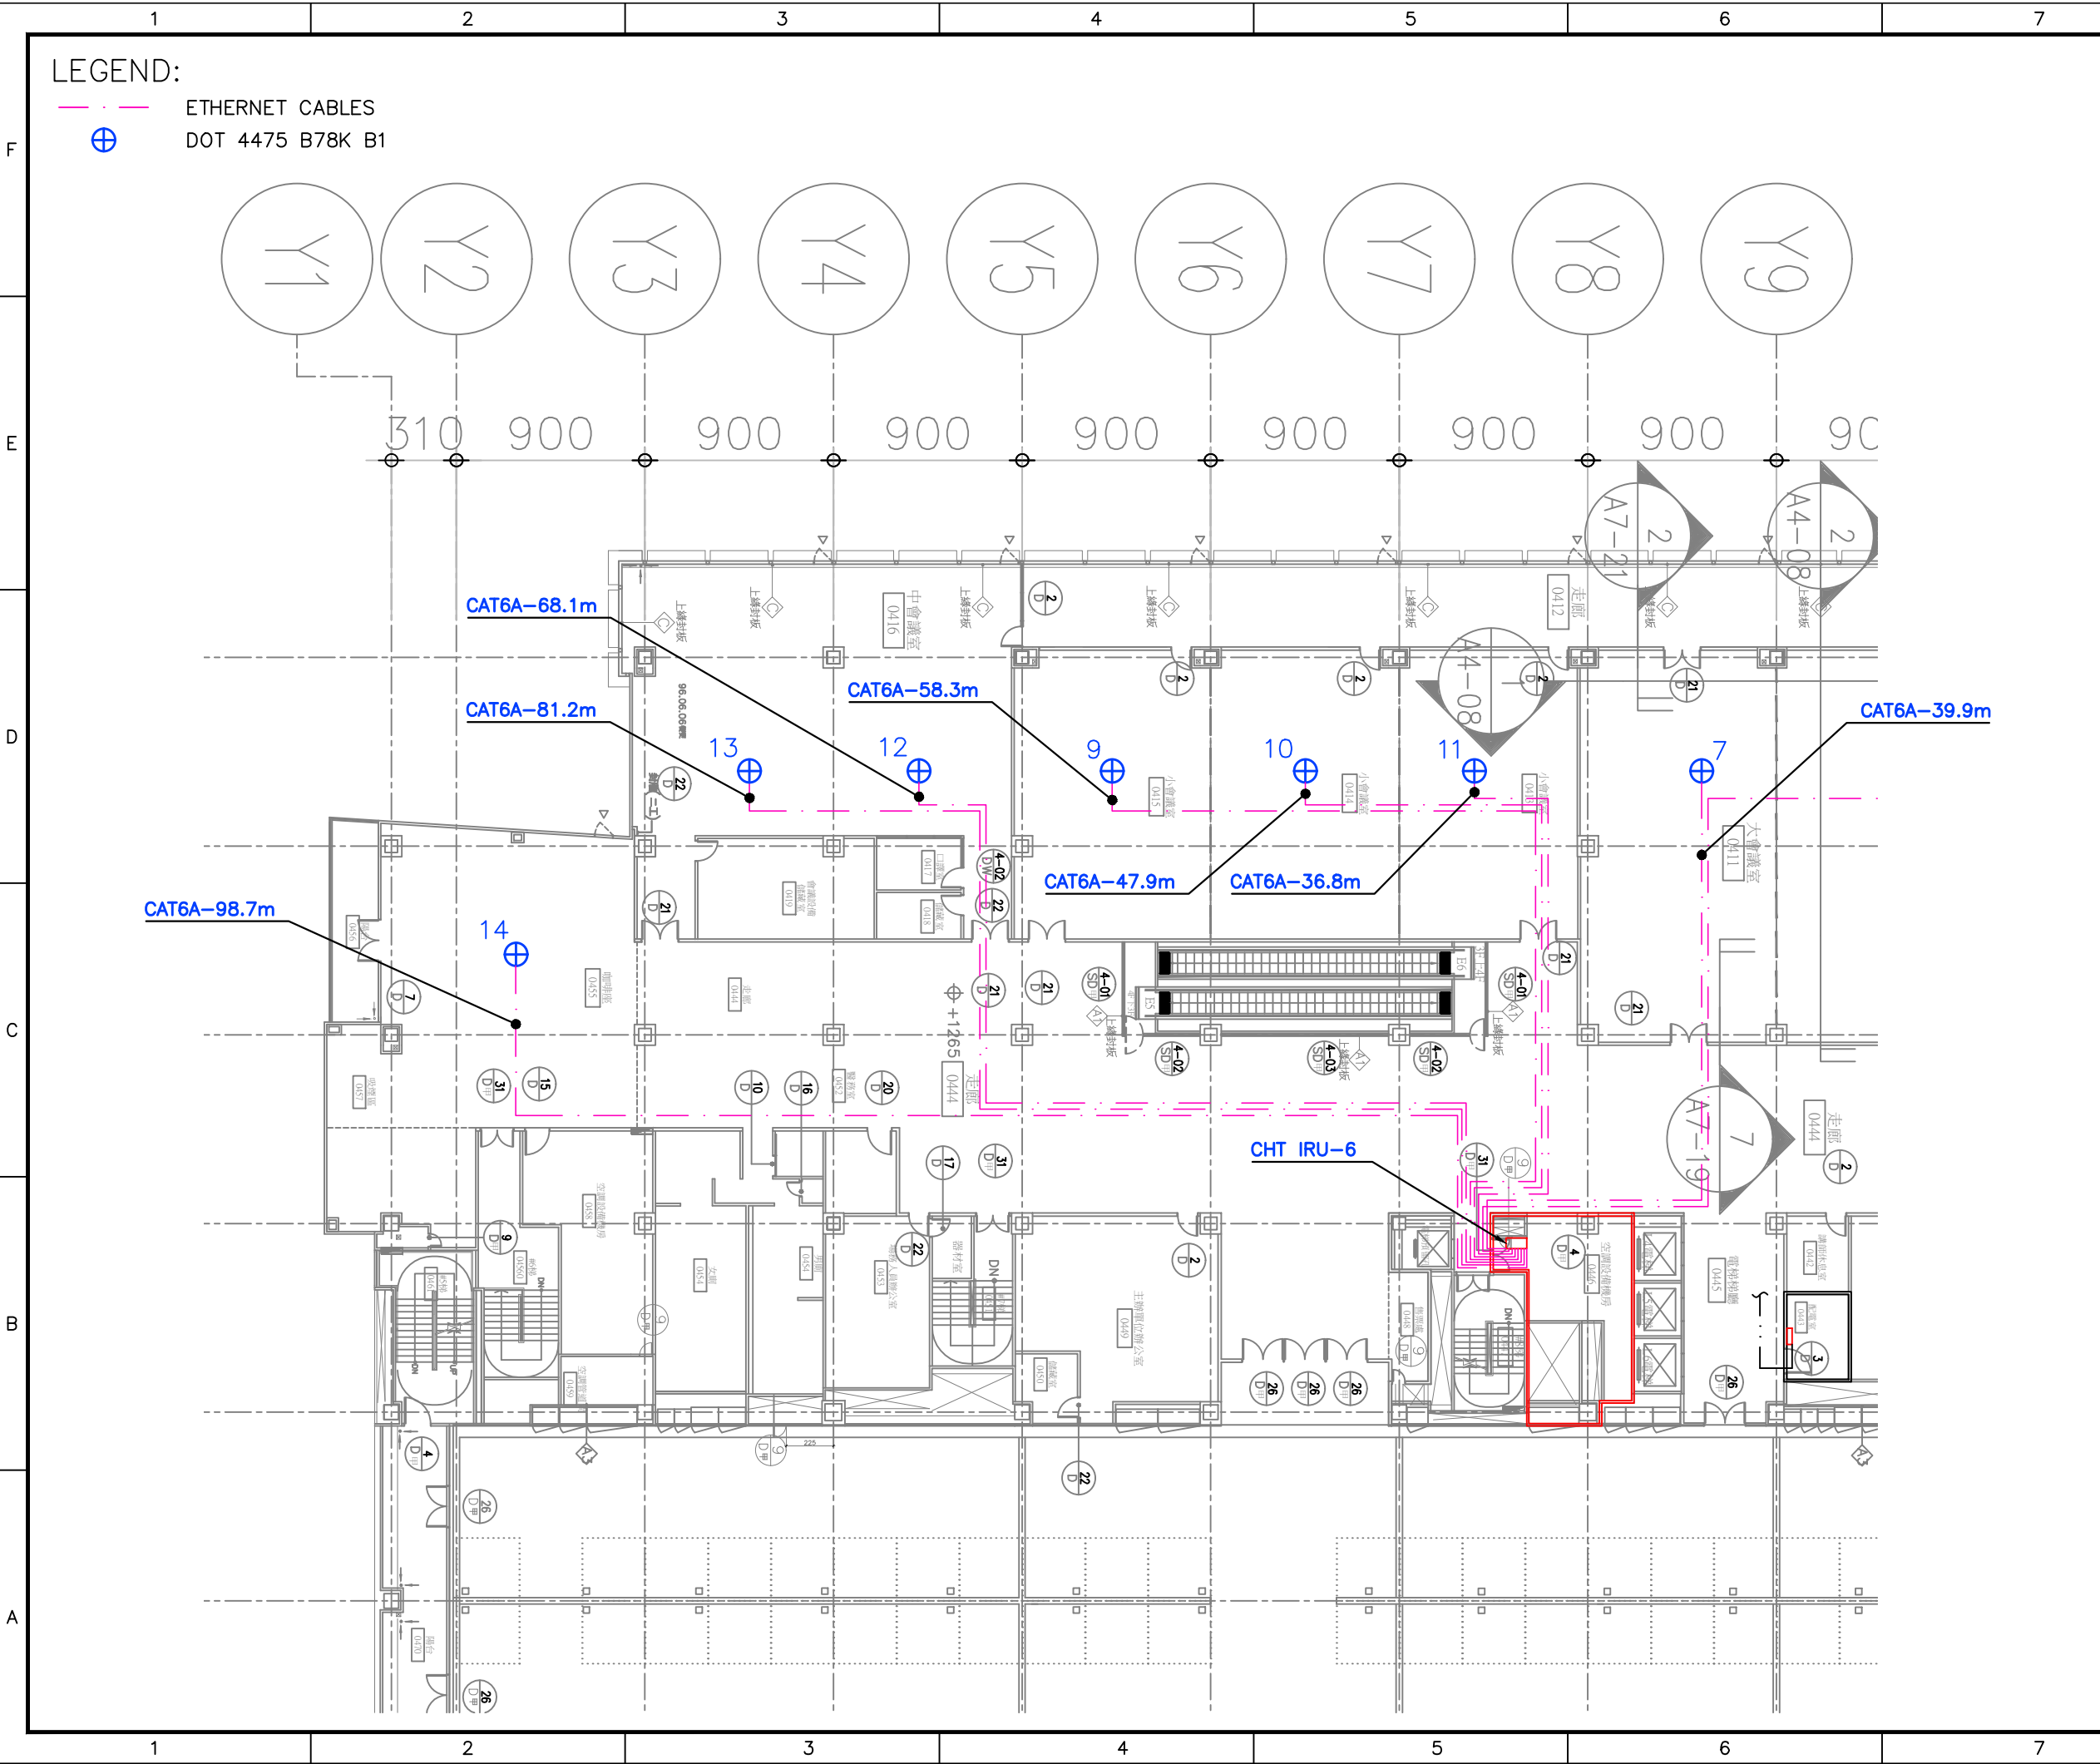


LEGEND:

ETHERNET CABLES


DOT 4475 B78K B1

版次	日期	修改	核准
中華電信股份有限公司 Chunghwa Telecom Co.,Ltd			
站台名稱 南港展館一館			
站台編號			
站台地址 臺北市南港區三重里 經貿二路1 號			
東經 E: 121.61811° 北緯 N: 25.05622°			
ERICSSON			
圖名: 四層平面圖(三)			
中華電信審圖工程師 APPROVED			
繪圖 DRAWN Kelly Chen			
日期 DATE 22/05/17		核發 DATE	
比例 SCALE 1: 300		單位 UNIT m	
頁數 SHEET 3		總頁 OF 4	
圖號 DRAWING NO.			

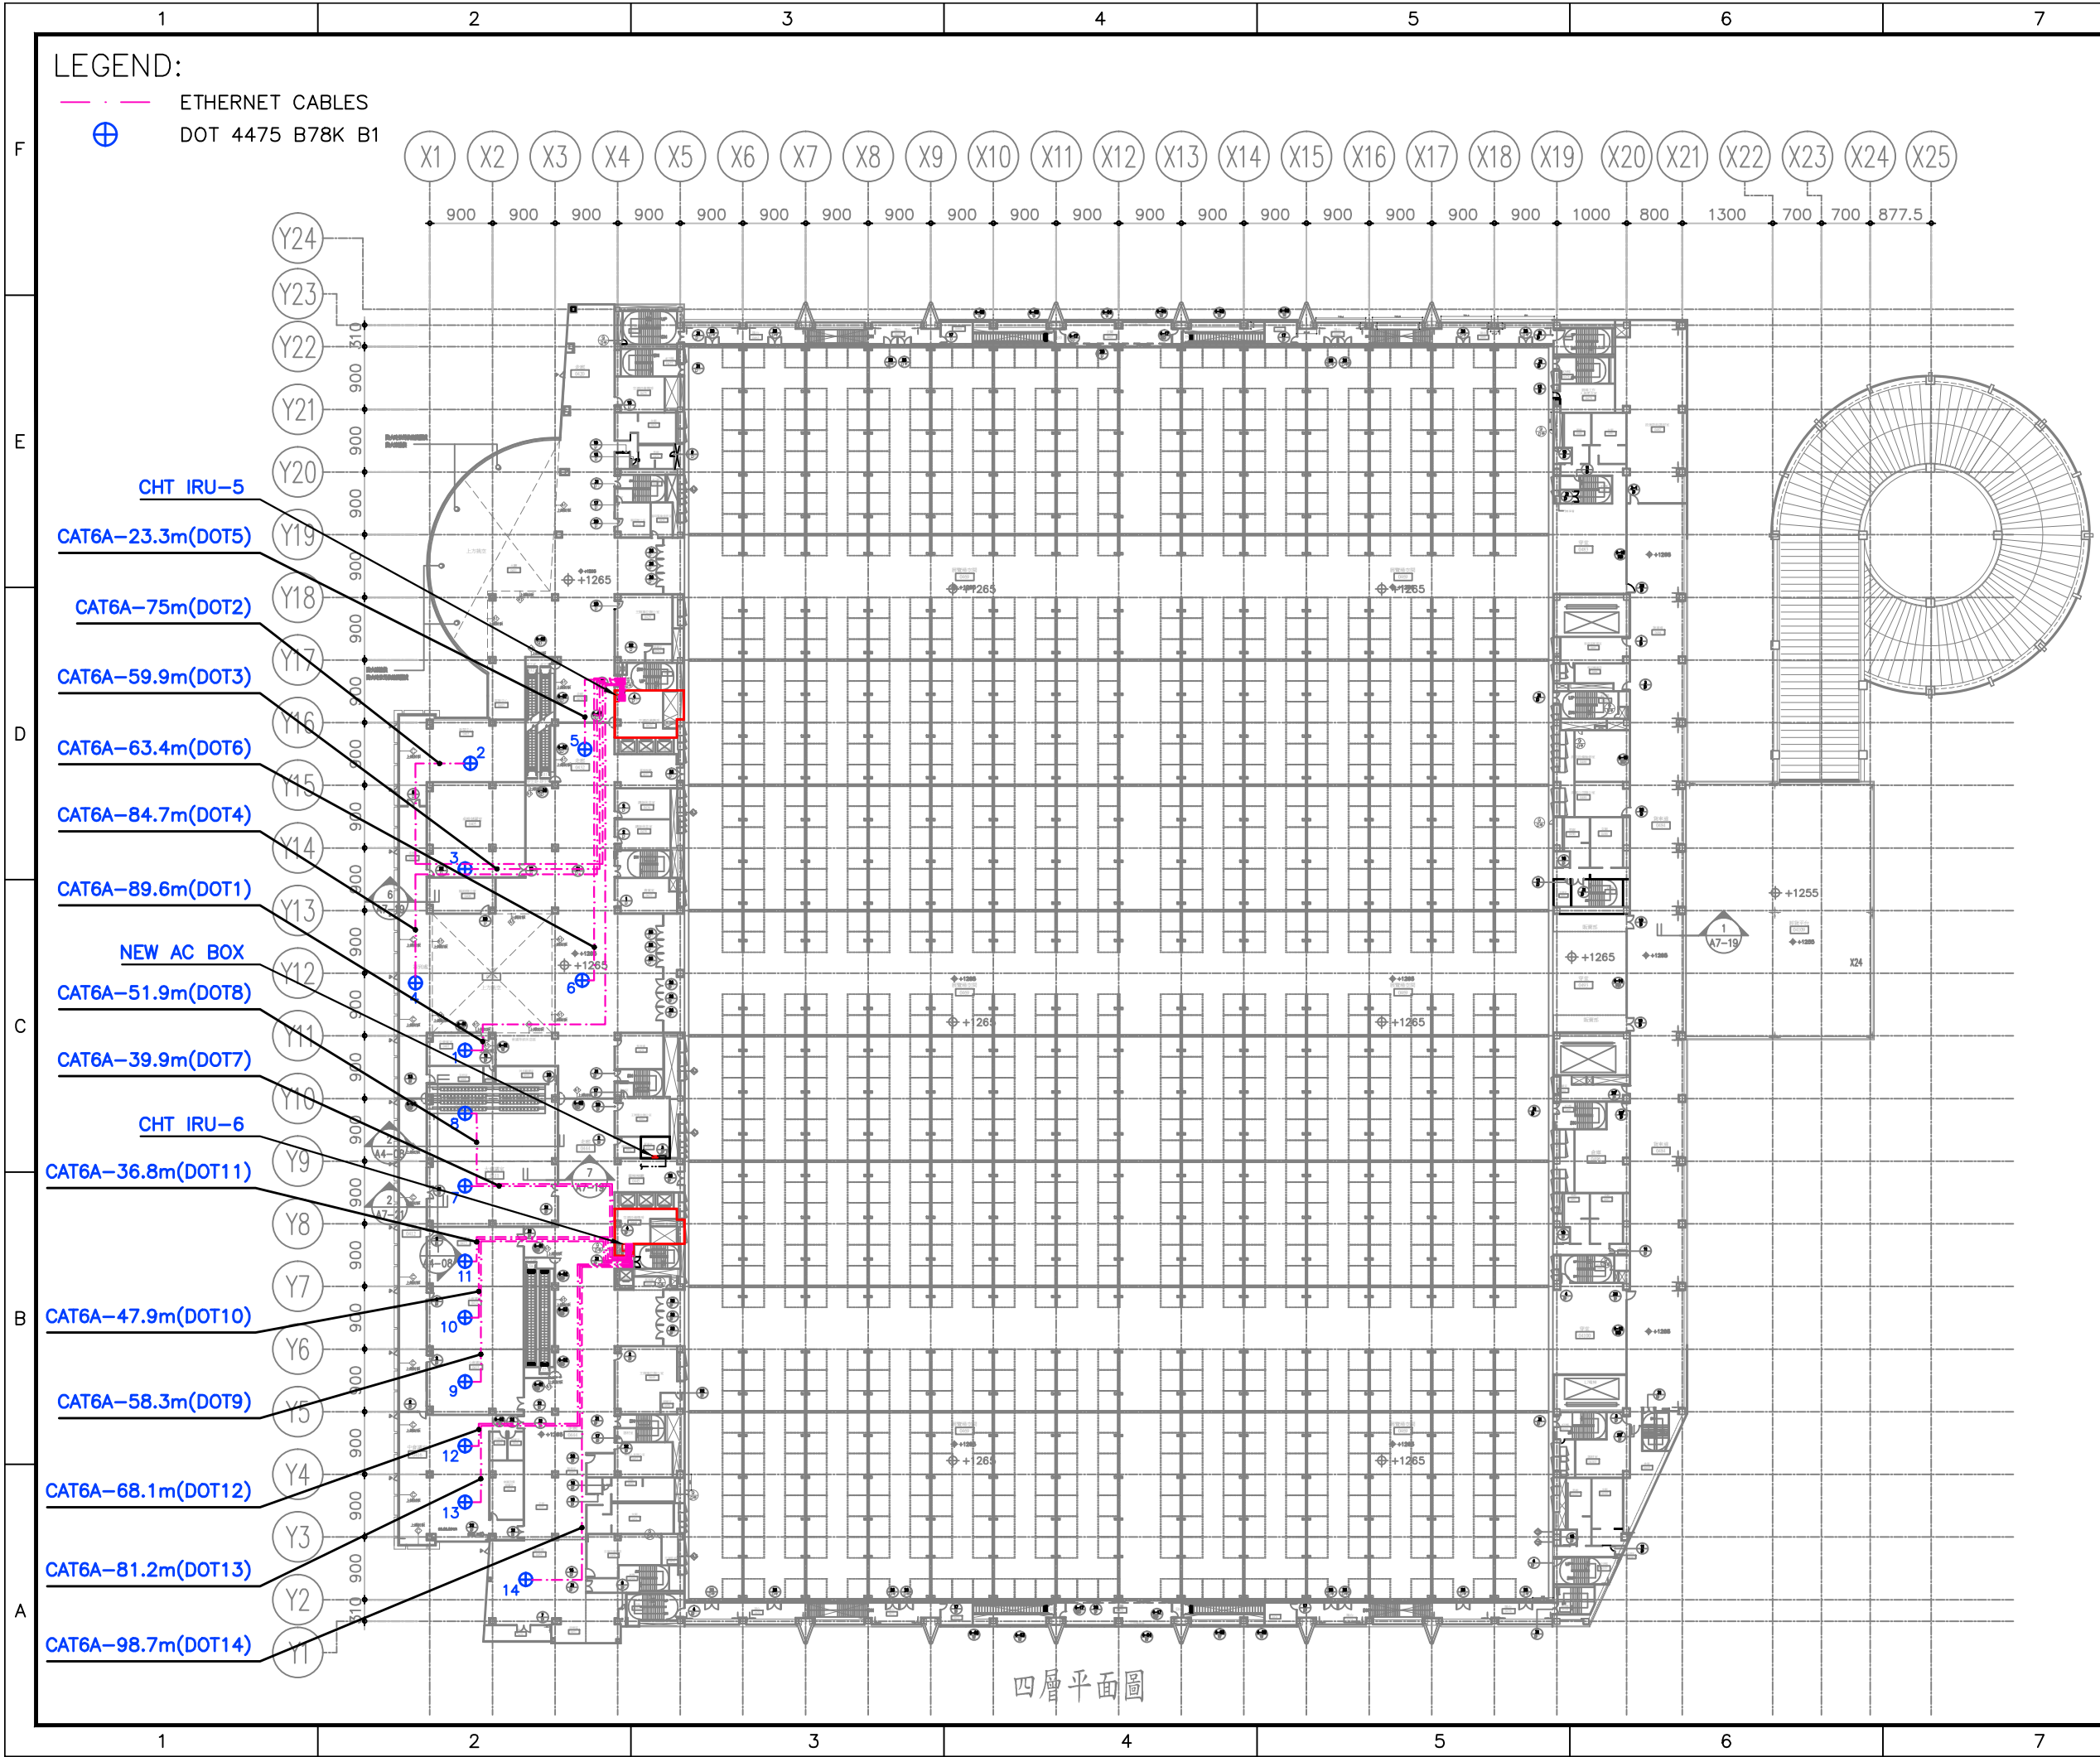

LEGEND:
ETHERNET CABLES
DOT 4475 B78K B1

版次	日期	修改	核准

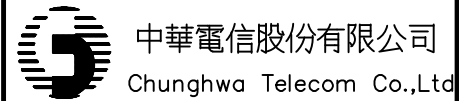

站名 南港展館一館
站編號
站地址 臺北市南港區三重里
經貿二路1 號

東經 E: 121.61811°
北緯 N: 25.05622°



圖名: 四層平面圖(全區)

中華電信審圖工程師
APPROVED

繪圖
DRAWN Kelly Chen

日期 DATE 22/05/17	核發 DATE
---------------------	------------

比例 SCALE 1:900	單位 UNIT m
-------------------	--------------

頁數 SHEET 4	總頁 OF 4
---------------	------------

圖號
DRAWING NO.

四層平面圖